


Total areas		
	Footprint 1	7,203 SF
	Net area 31	6,542 SF
	Doors area 25	51 SF
	Gross area 29	7,262 SF
	Gross Internal Area ...	306,823 SF
Total lines		
	Doors centerline 25	76 FT
	Wall centerline 160	1,030 FT
	Wall Perimeter 31	1,472 FT
Total counts		
	Toilet 5	5 EA
	Sink 5	5 EA
	Single Swing Door 25	25 EA
	Double Swing Door 11	11 EA
	Urinals 1	1 EA
	Cooktop 1	1 EA

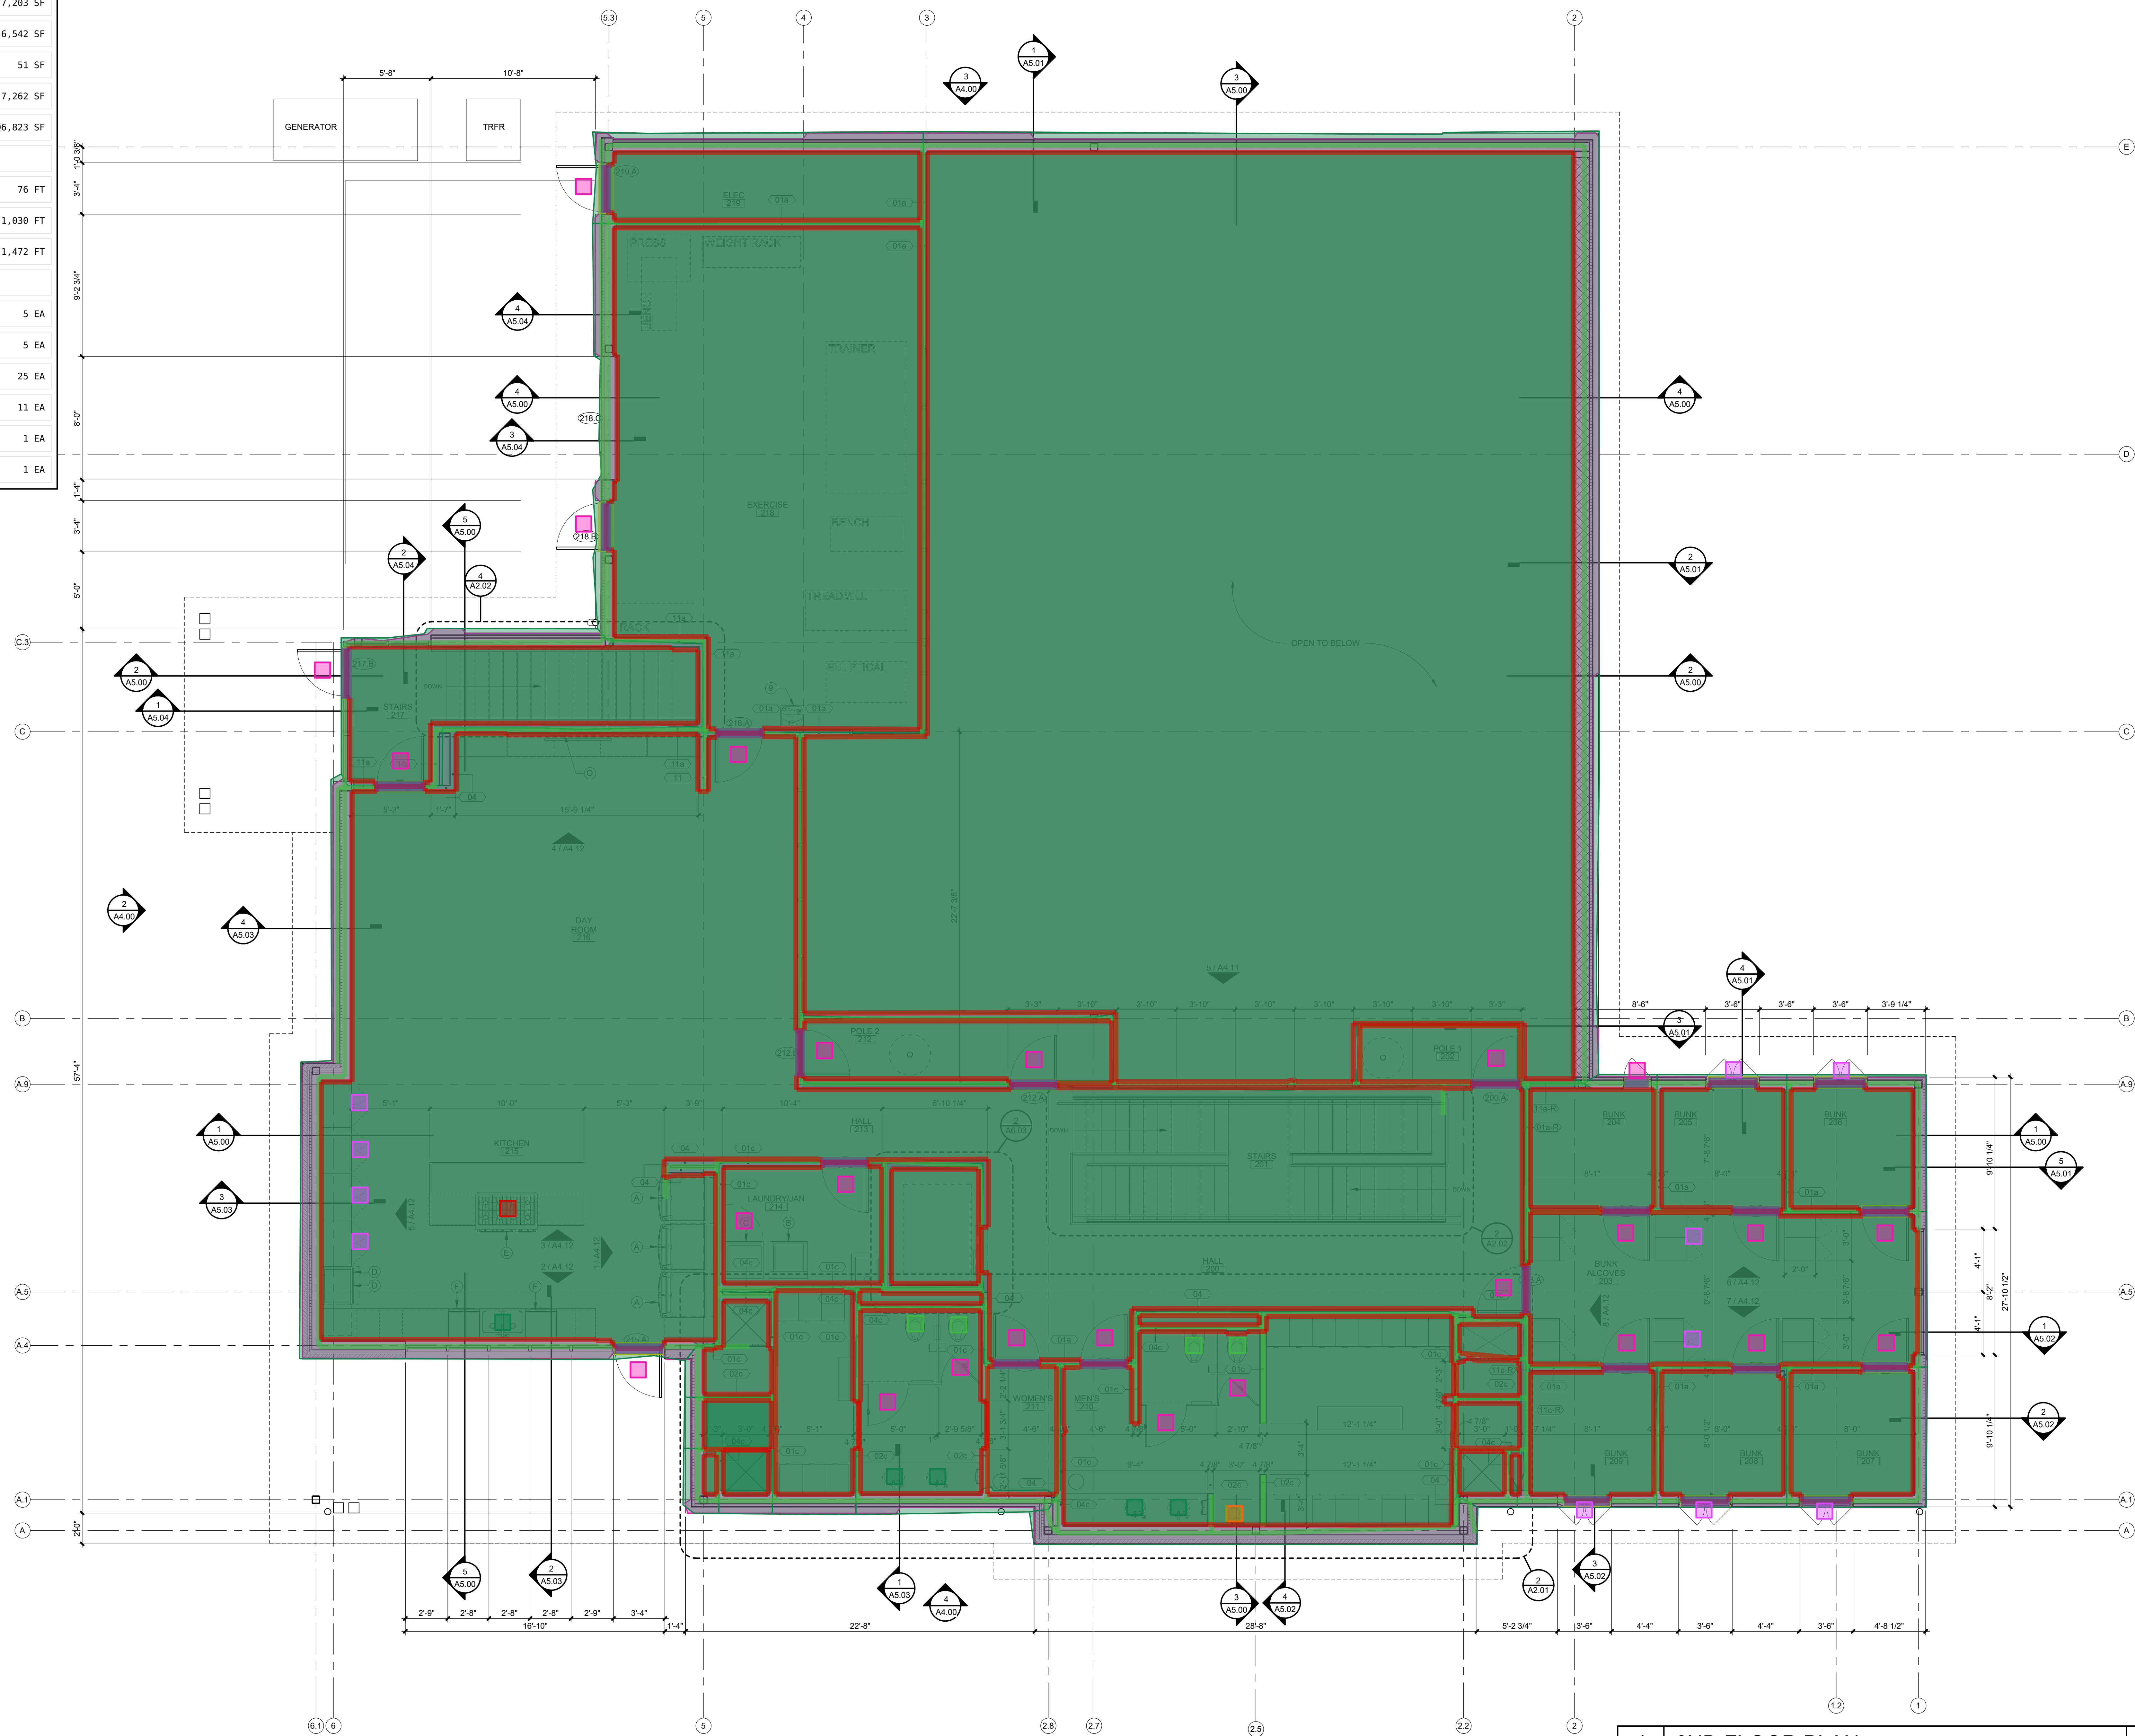

Olathe Fire
Station No. 8
14700 Lakeshore Dr
Olathe KS



Project No.:	19003
Date:	02.17.2020
Issued For:	DESIGN DEVELOPMENT

[illegible]

REGISTRATION

NOT FOR CONSTRUCTION

PROJECT TEAM

ARCHITECT FINKLE+WILLIAMS
ARCHITECTURE

FIRE STATION
CONSULTANT

CIVIL SK DESIGN GROUP

LANDSCAPE SWT DESIGN

STRUCTURAL BOB D. CAMPBELL

PLUMBING LANKFORD | FENDLEY

MECHANICAL LANKFORD | FENDU

ELECTRICAL LANKFORD | FENDL

CONTRACTOR TURNER CONSTRUCTION

FINKLE + WILLIAMS
ARCHITECTURE

7007 College Blvd, Suite 411
Overland Park, Kansas 66211
913+498-1550

SHEET TITLE

SECOND FLOOR
PLAN

SHEET NUMBER

A1.02